



RUMAH TYPE 36





TAMPAK KIRI





TAMPAK ATAS





TAMPAK BELAKANG







TAMPAK DEPAN





TAMPAK KANAN

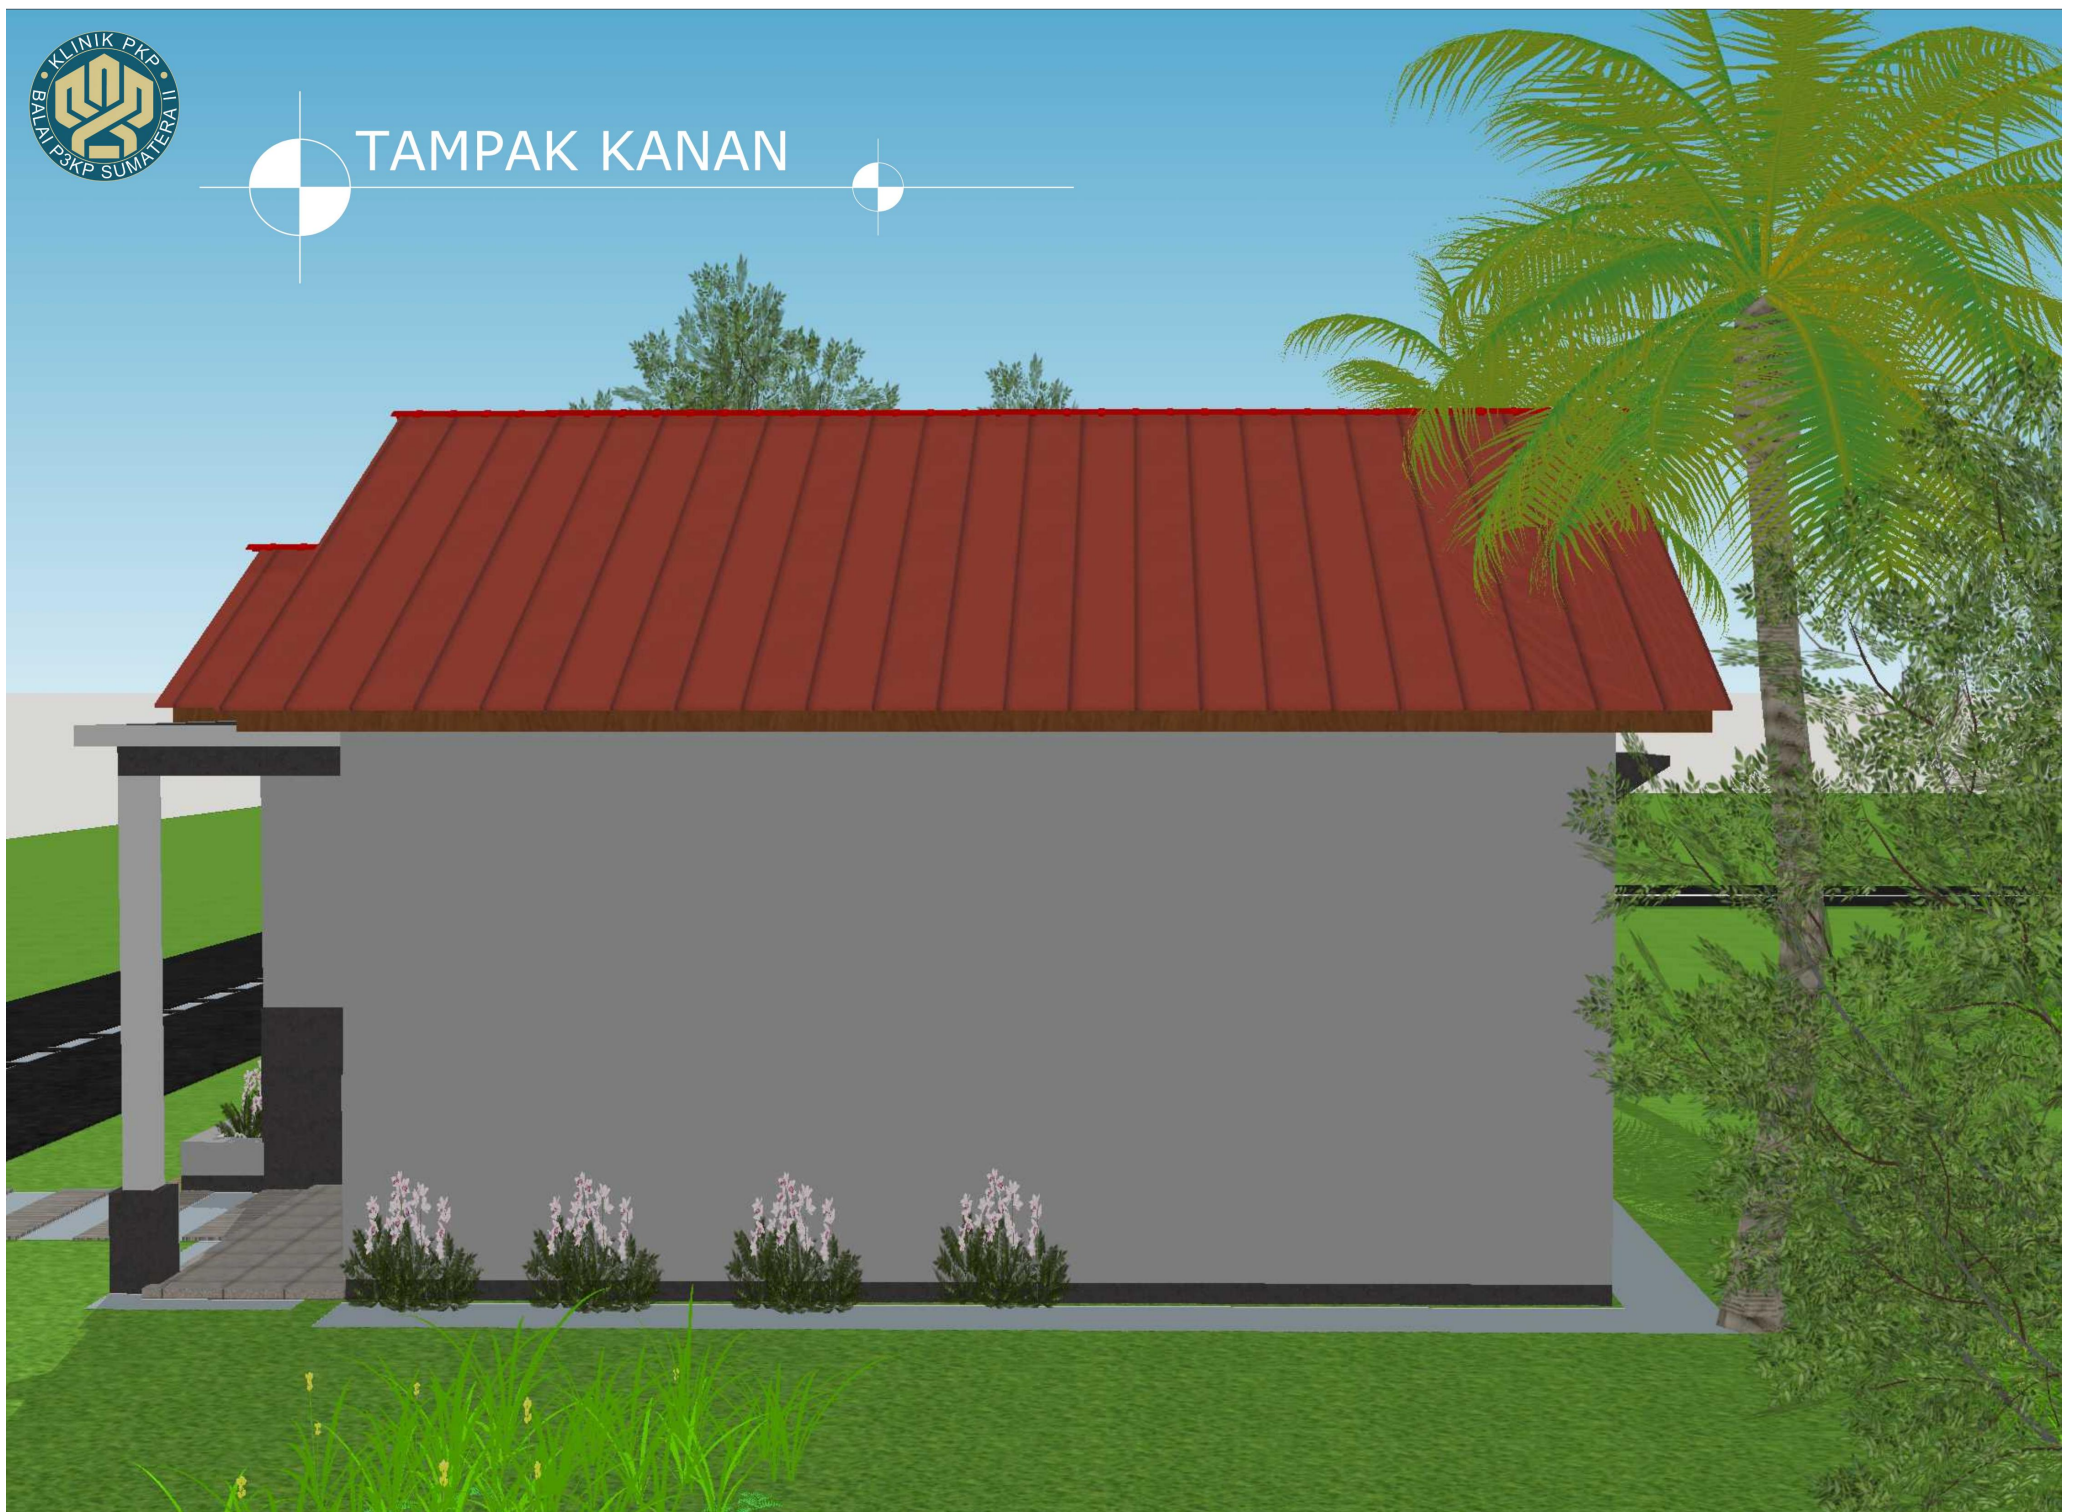


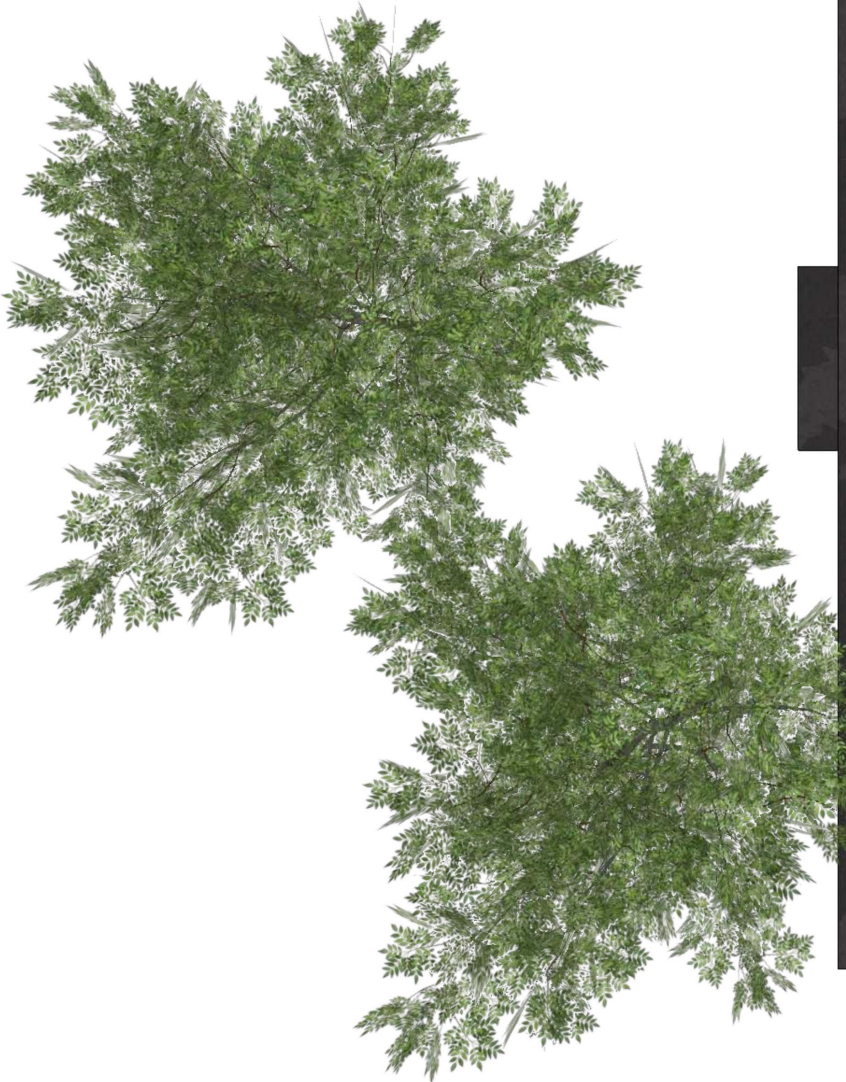






RANGKA ATAP



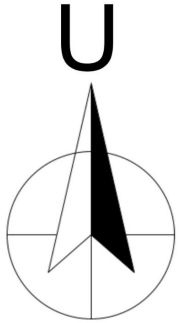

SKALA 1:100

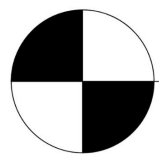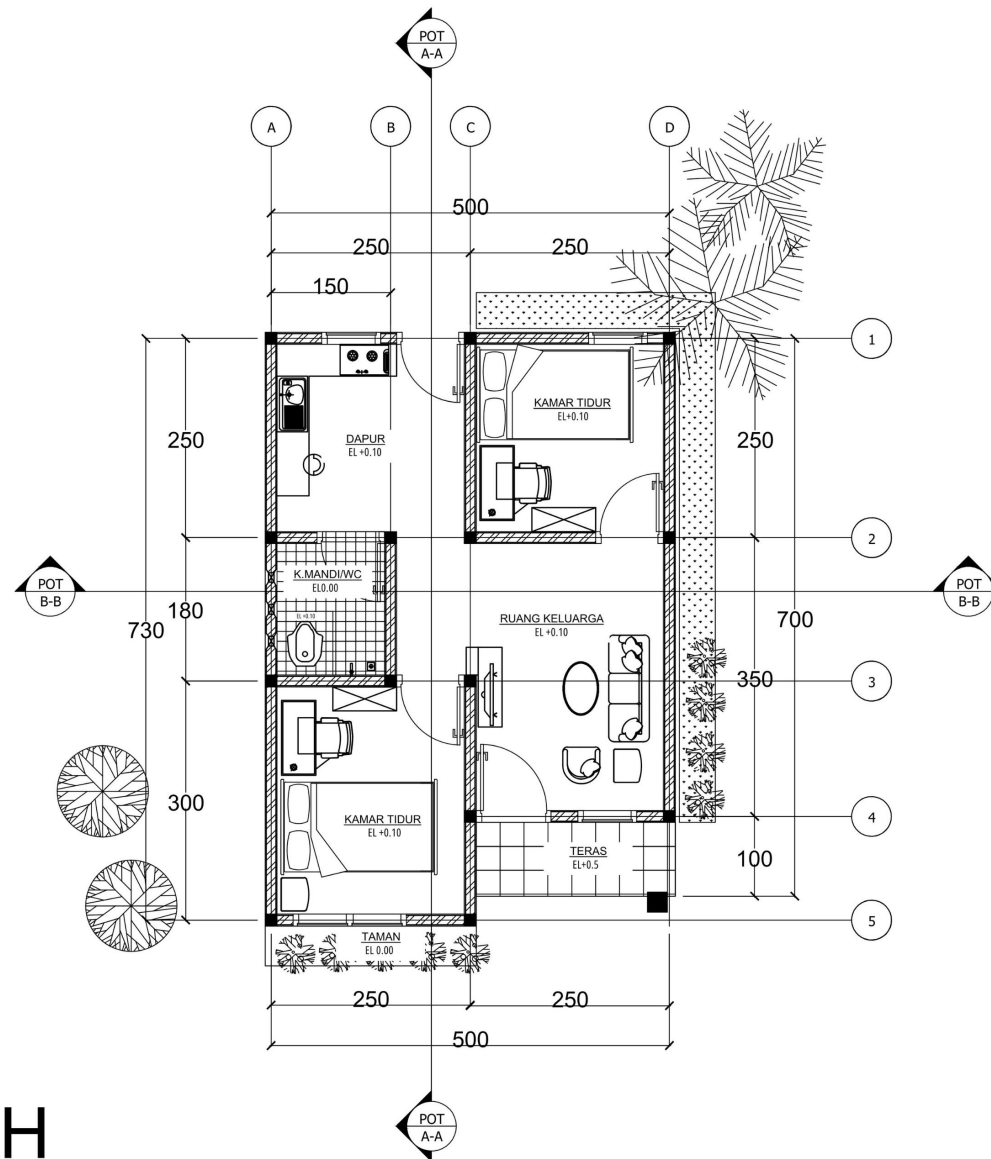
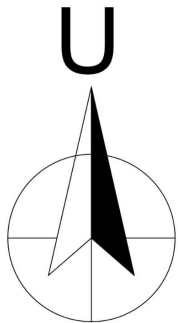


DENAH

SKALA 1:100






U

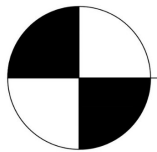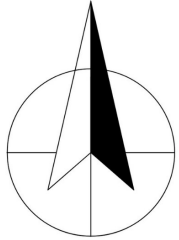




TAMPAK DEPAN

SKALA 1:100

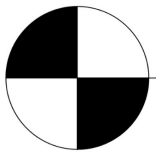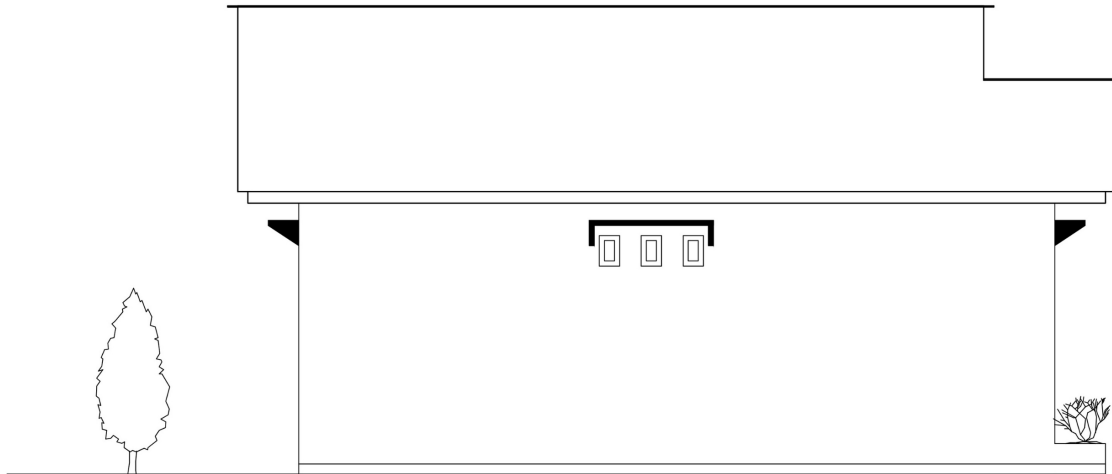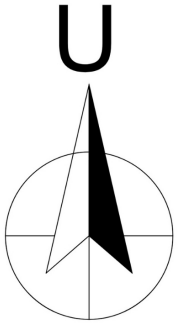




TAMPAK KANAN

SKALA 1:100

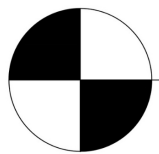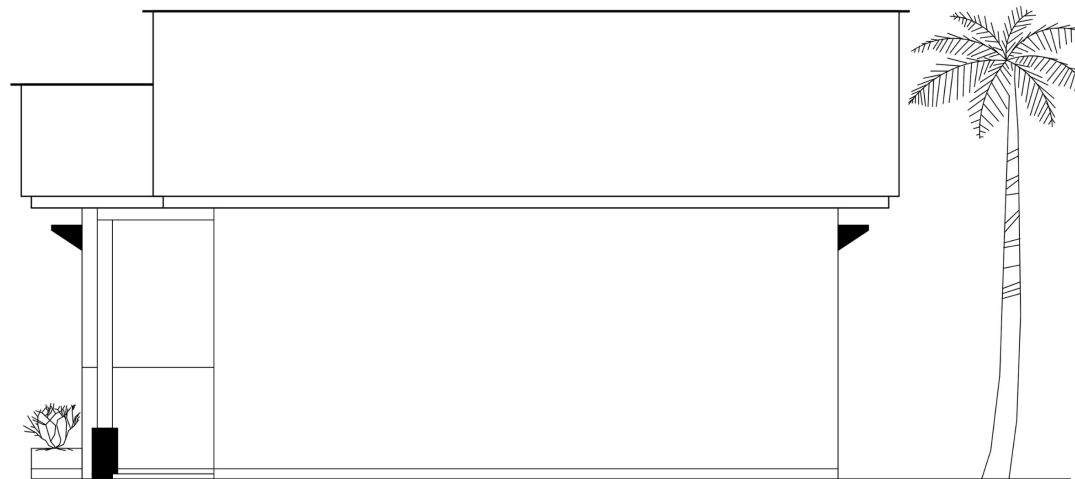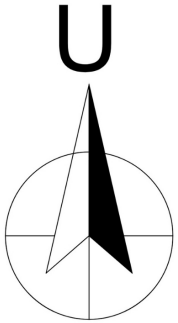




TAMPAK KIRI

SKALA 1:100

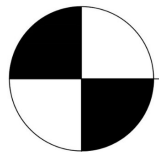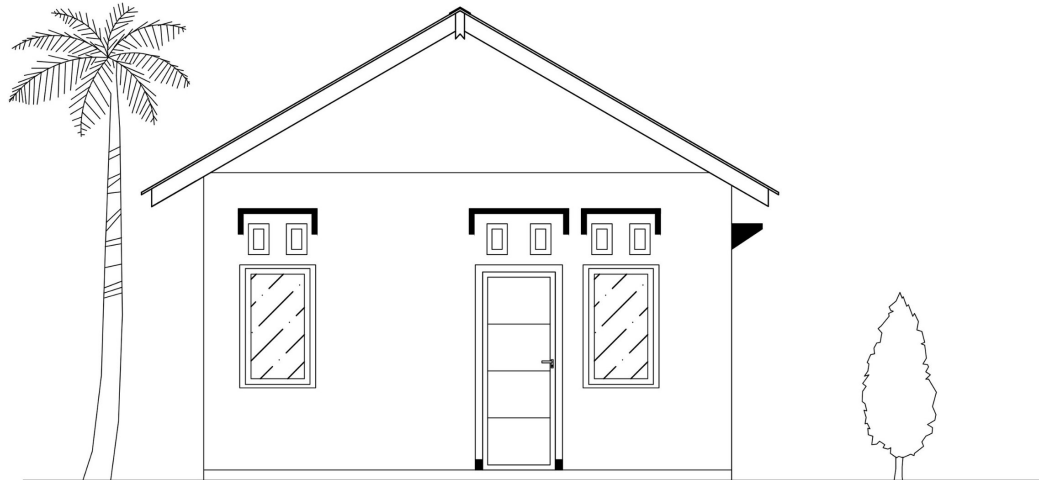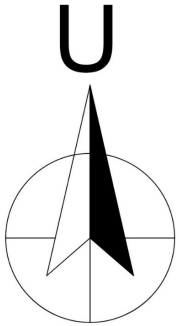


TAMPAK BELAKANG

SKALA 1:100

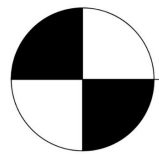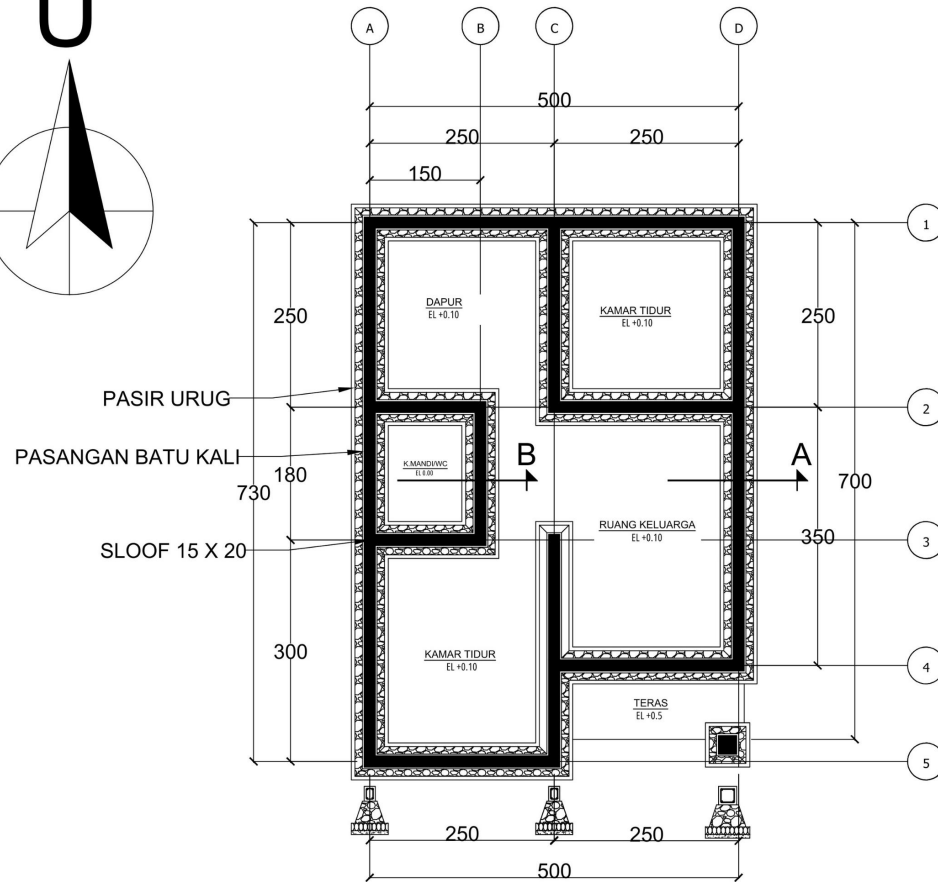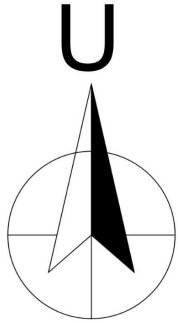


RENCANA PONDASI

SKALA 1:100

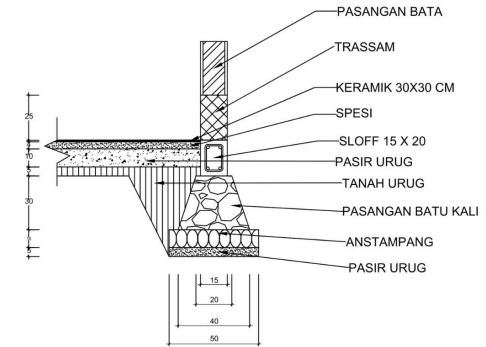




DETAIL POT A

SKALA 1:50

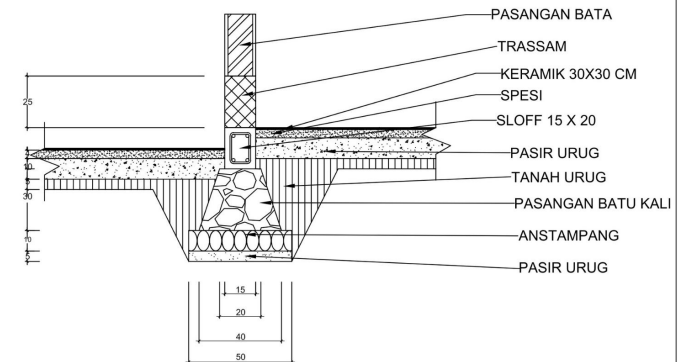

DETAIL POT B

SKALA 1:50

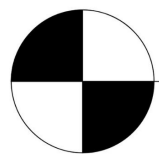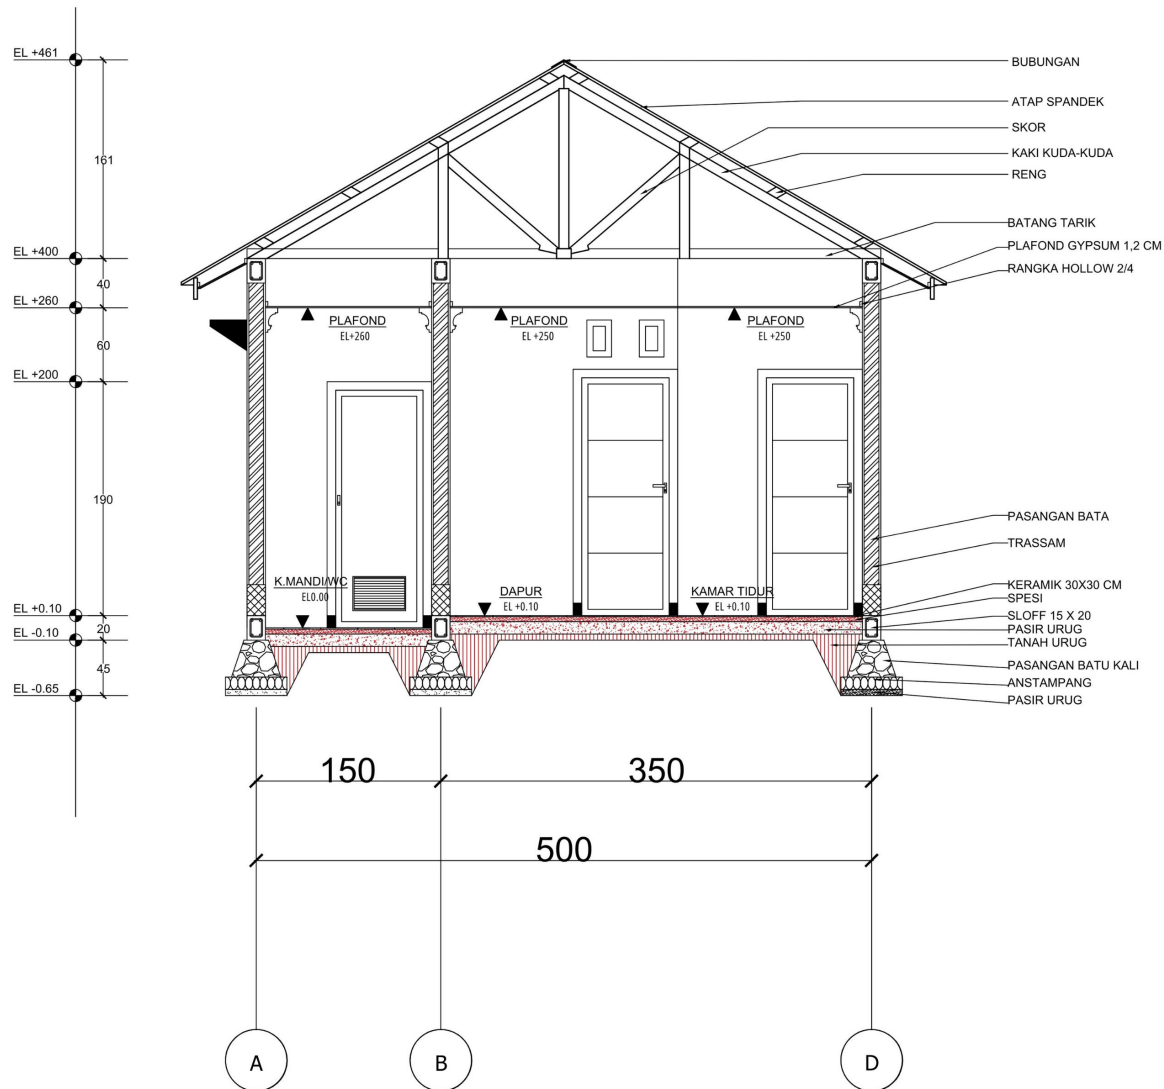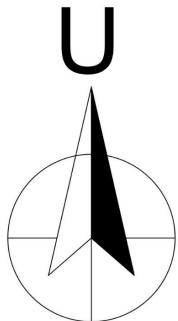

POTONGAN B-B

SKALA 1:100